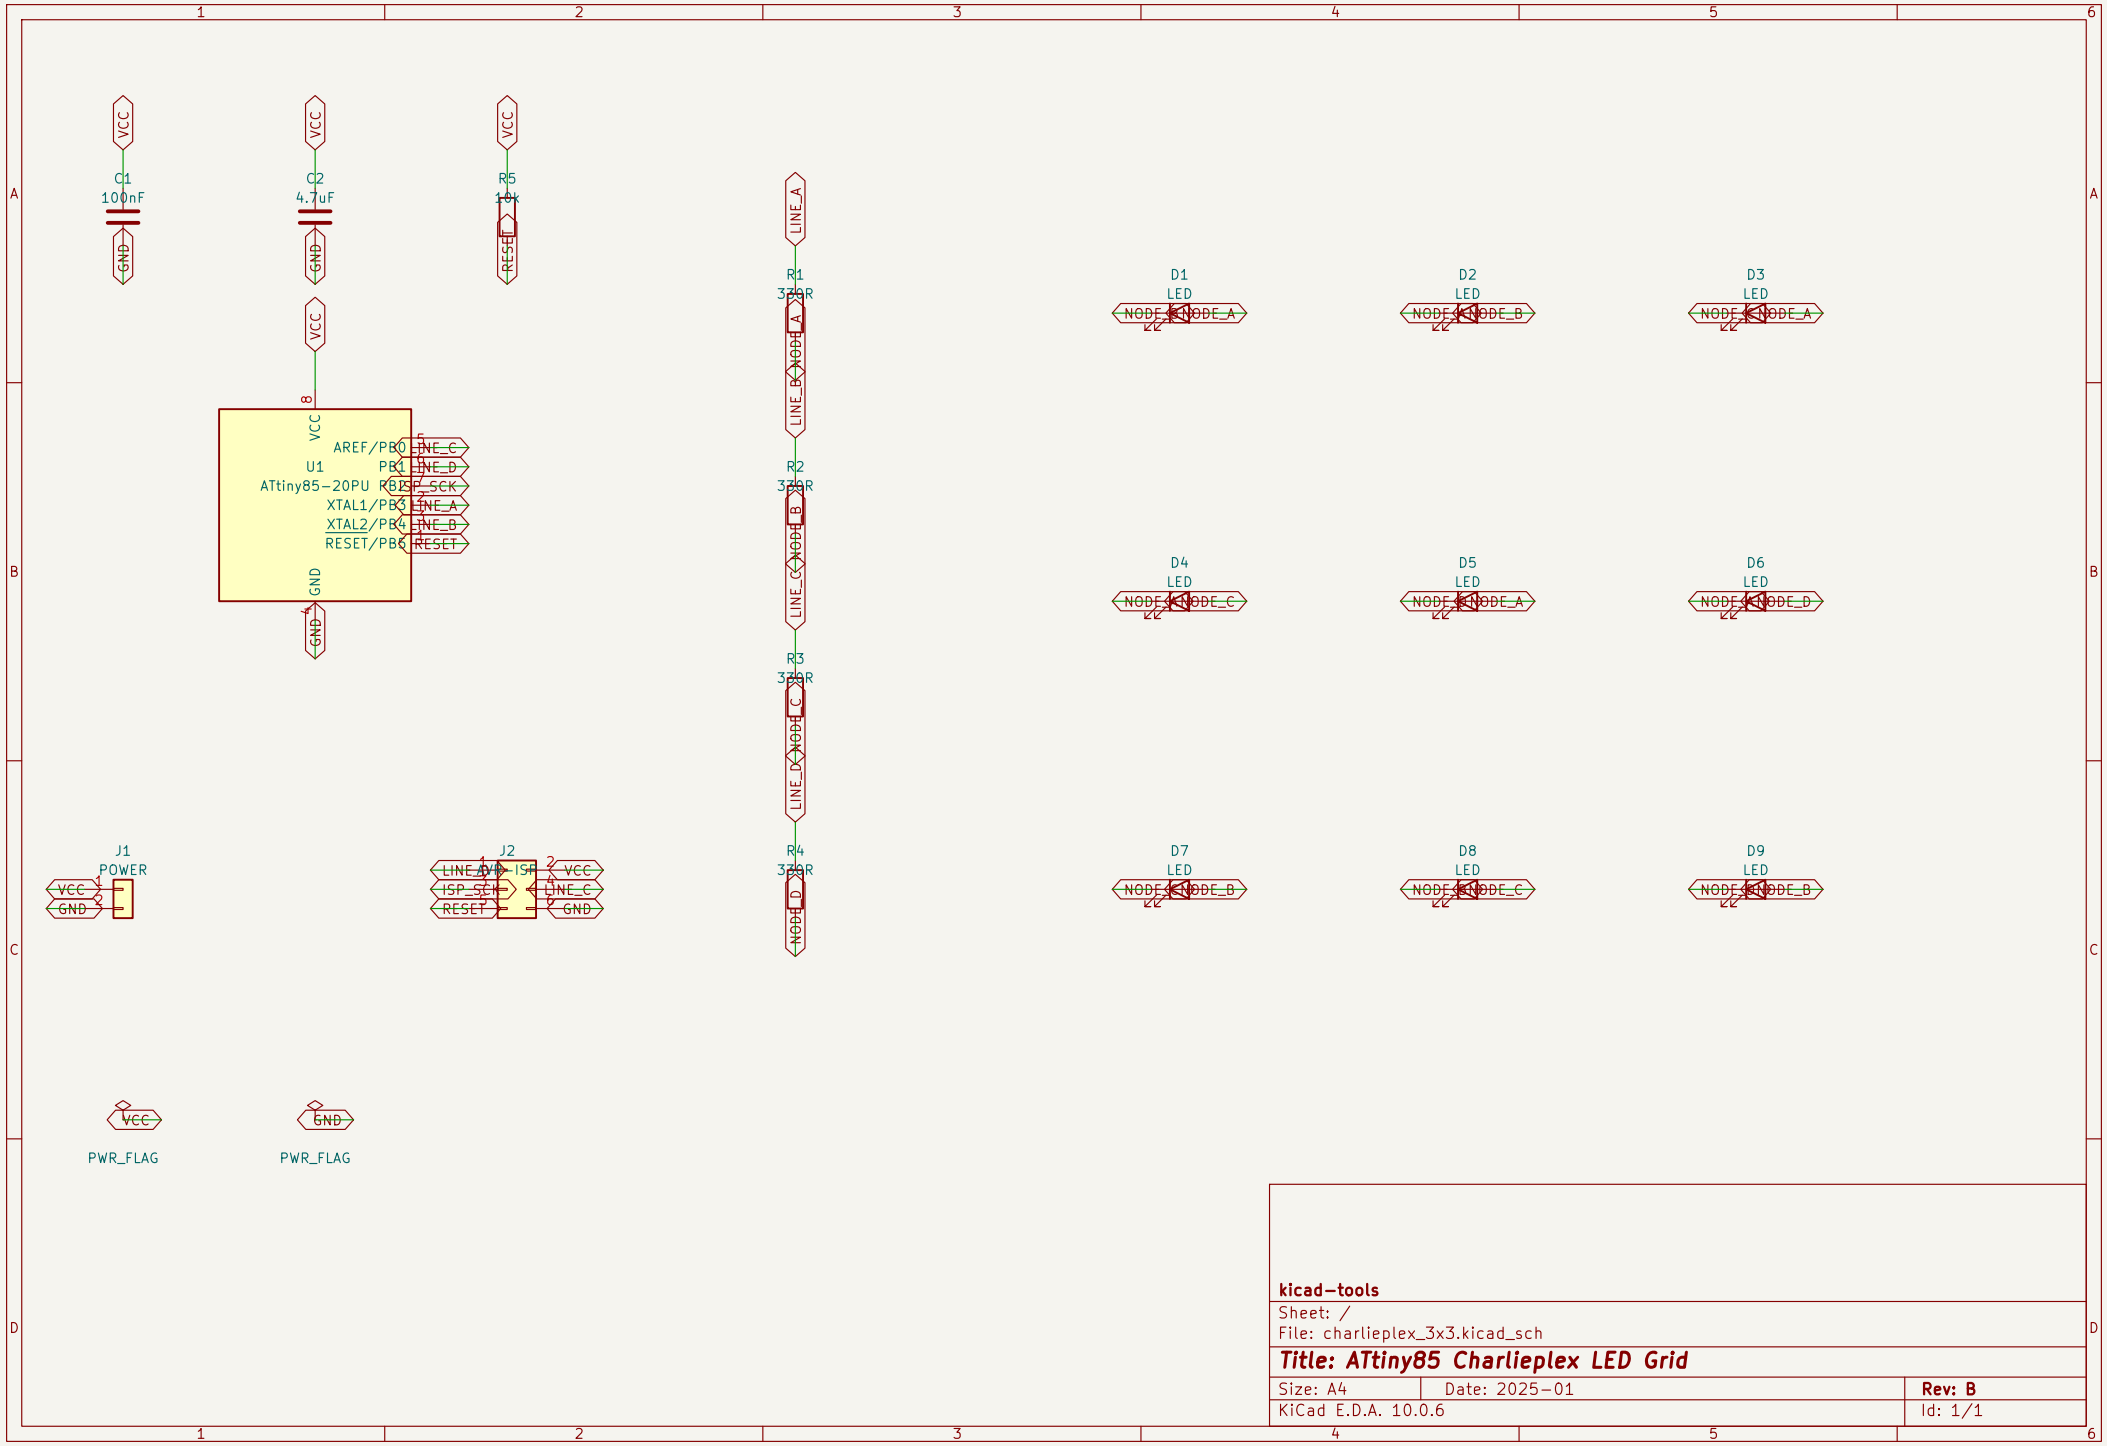

C1
100nF
C2
4.7uF
R5
10K
VCC
GND
RESET
U1
ATtiny85-20PU
AREF/PB0
PB1
PB2
XTAL1/PB3
XTAL2/PB4
RESET/PB5
LINE_C
LINE_D
ISP_SCK
LINE_A
LINE_B
R1
R2
R3
R4
330R
LINE_A
LINE_B
LINE_C
LINE_D
D1
D2
D3
D4
D5
D6
D7
D8
D9
LED
J1
POWER
J2
ISP
PWR_FLAG
kicad-tools
Sheet: /
File: charlieplex_3x3.kicad_sch
Title: ATtiny85 Charlieplex LED Grid
Size: A4
Date: 2025-01
Rev: B
KiCad E.D.A. 10.0.6
Id: 1/1